
MODULE TYPE, DIMENSIONS & WEIGHT


NUMBER OF MODULES = 23 MODULES
MODULE TYPE = SIRIUS SOLAR ELNSM54M-HC-N 450W MONO MODULES
MODULE WEIGHT = 47.39 LBS / 21.5KG.
MODULE DIMENSIONS = 67.80" x 44.65" = 21.02 SF

ROOF ARRAY AREA #1:- 210.20 SQ FT.
ROOF ARRAY AREA #2:- 273.26 SQ FT.

NOTE:
1. NON-HABITIABLE STRUCTURE DOES NOT REQUIRE FIRE SETBACK.
2. PURLIN SIZE AND SPACING OF DETACHED STRUCTURE TO BE 24" WITH 2"X4" SIZE.

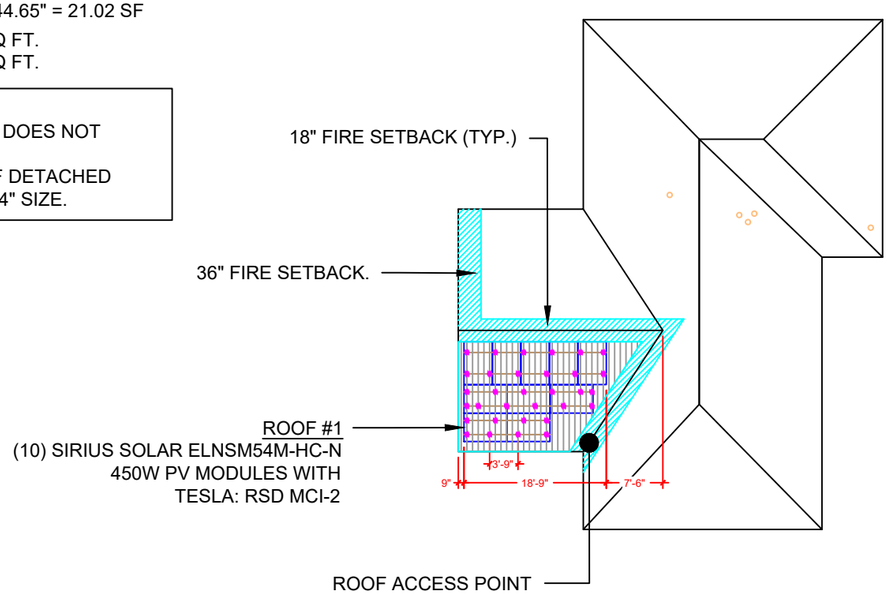



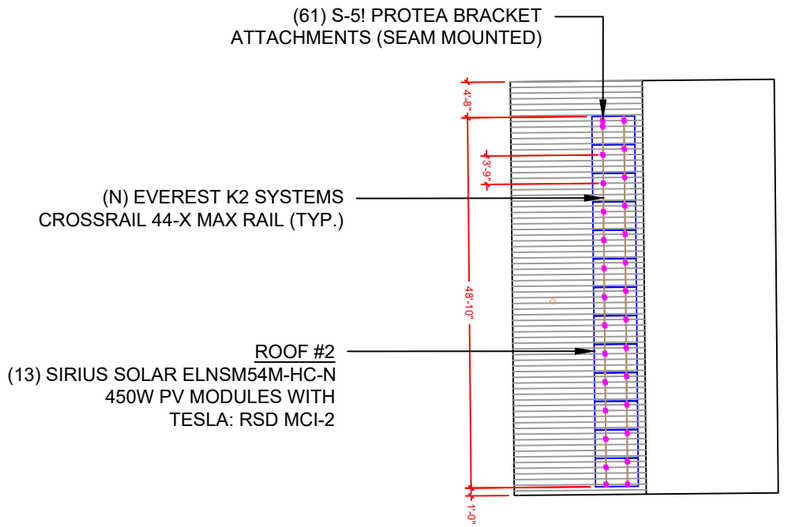

ROOF DESCRIPTION

ROOF TYPE				METAL ROOF			CONFIGURATION
ROOF	# OF MODULES	ROOF PITCH	AZIMUTH	RAFTER SIZE	RAFTER SPACING	SEAM SPACING	
#1	10	17°	180°	2"X6"	16"	9"	STAGGERED

ROOF DESCRIPTION

ROOF TYPE				METAL ROOF			CONFIGURATION
ROOF	# OF MODULES	ROOF PITCH	AZIMUTH	TRUSS SIZE	TRUSS SPACING	SEAM SPACING	
#2	13	13°	269°	2"X8"	106"	9"	STAGGERED

BILL OF MATERIALS


EQUIPMENT	QTY	DESCRIPTION
SOLAR PV MODULES	23	SIRIUS SOLAR ELNSM54M-HC-N 450W
MCI's	09	TESLA: RSD MCI-2
INVERTER/BATTERY	01	TESLA POWERWALL 3 (1707000-XX-Y)
EXPANSION	01	TESLA POWERWALL 3 EXPANSION (1807000-xx-y)
TESLA BACKUP SWITCH	1	TESLA BACKUP SWITCH (1624171-xx-y)
RSD	01	IMO RAPID SHUTDOWN SWITCH (PE69-3020)
RAILS	15	EVEREST K2 SYSTEMS CROSSRAIL 44-X MAX RAIL
SPLICE	10	SPLICE KIT
MODULE CLAMPS	38	MID MODULE CLAMPS
END CLAMPS	16	END CLAMPS
ATTACHMENT	61	S-5! PROTEA BRACKET ATTACHMENTS (SEAM MOUNTED)
DC DISCONNECT	1	DC DISCONNECT , 32A/600V, 4 POLE
PHOTOVOLTAIC/ENERGY STORAGE SYSTEM AC DISCONNECT	01	60A FUSED PHOTOVOLTAIC/ENERGY STORAGE SYSTEM AC DISCONNECT 240V NEMA 3R, UL LISTED (D222NRB)

ARRAY AREA & ROOF AREA CALC'S (MAIN HOUSE)

TOTAL PV ARRAY AREA (SQ. FT.)	TOTAL ROOF AREA (Sq. Ft.)	ROOF AREA COVERED BY ARRAY (%)
210.20	2897.46	7

ARRAY AREA & ROOF AREA CALC'S (DETACHED STRCTURE)

TOTAL PV ARRAY AREA (SQ. FT.)	TOTAL ROOF AREA (Sq. Ft.)	ROOF AREA COVERED BY ARRAY (%)
273.26	1901.310	14

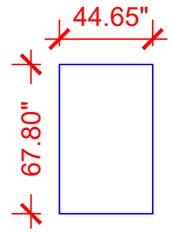

SIRIUS SOLAR
ELNSM54M-HC-N
450W MODULES

LEGEND

- VENT, ATTIC FAN (ROOF OBSTRUCTION)
- ROOF ATTACHMENT
- RAIL
- SEAM

1 ROOF PLAN AND MODULES

PV-3 SCALE: 1"=20'-0"

TRON SOLAR LLC.
CONTRACTOR ADDRESS:
950 CORPORATE WOODS PARKWAY,
VERNON HILLS, IL 60061
LICENSE #. TGC110144

REVISIONS		
DESCRIPTION	DATE	REV
INITIAL	07/20/2026	
REVISION	07/28/2026	A
REVISION	10/12/2026	B

PROJECT NAME & ADDRESS
SYLVIA MOYES RESIDENCE
308 S 3RD ST,
SAINT FRANCISVILLE, IL 62460
(38.589233, -87.643491)

DRAWN BY
ESR

SHEET NAME
ROOF PLAN AND MODULES

SHEET SIZE
ANSI B
11" X 17"

SHEET NUMBER
PV-3