MODULE TYPE, DIMENSIONS & WEIGHT


NUMBER OF MODULES = 42 MODULES
MODULE TYPE = SIRIUS SOLAR ELNSM54M-HC-N 450W MONO MODULES
MODULE WEIGHT = 47.39 LBS / 21.5KG.
MODULE DIMENSIONS = 67.80" x 44.65" = 21.02 SF

ROOF ARRAY AREA #1:- 315.30 SQ FT.
ROOF ARRAY AREA #2:- 315.30 SQ FT.
ROOF ARRAY AREA #3:- 252.24 SQ FT.

ARRAY AREA & ROOF AREA CALC'S-HOUSE		
TOTAL PV ARRAY AREA (SQ. FT.)	TOTAL ROOF AREA (Sq. Ft.)	ROOF AREA COVERED BY ARRAY (%)
630.60	1190.18	53



ROOF DESCRIPTION						
ROOF TYPE				ASPHALT SHINGLE		
ROOF	# OF MODULES	ROOF PITCH	AZIMUTH	TRUSS SIZE	TRUSS SPACING	SEAMS SPACING
#1	12	18°	170°	2"x6"	24"	9"

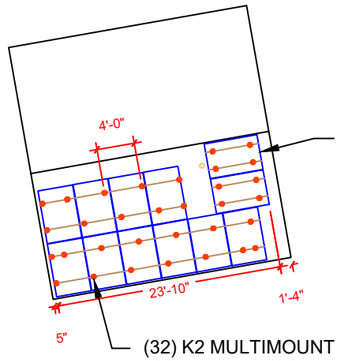



ROOF #3
(12) SIRIUS SOLAR ELNSM54M-HC-N 450W PV MODULES WITH TESLA: RSD MCI-2

(32) K2 MULTIMOUNT ATTACHMENTS (DECK MOUNTED)

ROOF DESCRIPTION						
ROOF TYPE				METAL ROOF		CONFIGURATION
ROOF	# OF MODULES	ROOF PITCH	AZIMUTH	RAFTER SIZE	RAFTER SPACING	
#1	15	44°	83°	2"X4"	22"	STAGGERED
#2	15	44°	263°	2"X4"	22"	STAGGERED

BILL OF MATERIALS		
EQUIPMENT	QTY	DESCRIPTION
SOLAR PV MODULES	42	SIRIUS SOLAR ELNSM54M-HC-N 450W
MCI's	14	TESLA: RSD MCI-2
INVERTER/BATTERY	02	TESLA POWERWALL 3 (1707000-xx-y)
EXPANSION	01	TESLA POWERWALL 3 EXPANSION (1807000-xx-y)
GATEWAY	01	TESLA BACKUP GATEWAY 3, 200A, NEMA 3R RATED, 120/240V (1841000-x1-y)
RSD	01	IMO RAPID SHUTDOWN SWITCH (PE69-3020)
RAILS	33	EVEREST K2 SYSTEMS CROSSRAIL 44-X MAX RAIL
SPLICE	16	SPLICE KIT
MODULE CLAMPS	56	MID MODULE CLAMPS
END CLAMPS	56	END CLAMPS
DC DISCONNECT	1	DC DISCONNECT, 32A/600V, 4 POLE
DC DISCONNECT	2	DC DISCONNECT, 32A/600V, 2 POLE
PHOTOVOLTAIC/ENERGY STORAGE SYSTEM AC DISCONNECT	02	60A NON-FUSED PHOTOVOLTAIC/ENERGY STORAGE SYSTEM AC DISCONNECT 240V NEMA 3R, UL LISTED (DU222RB)
ATTACHMENT	32	K2 MULTIMOUNT ATTACHMENTS (DECK MOUNTED)
ATTACHMENT	112	S-5! PROTEA BRACKET ATTACHMENTS

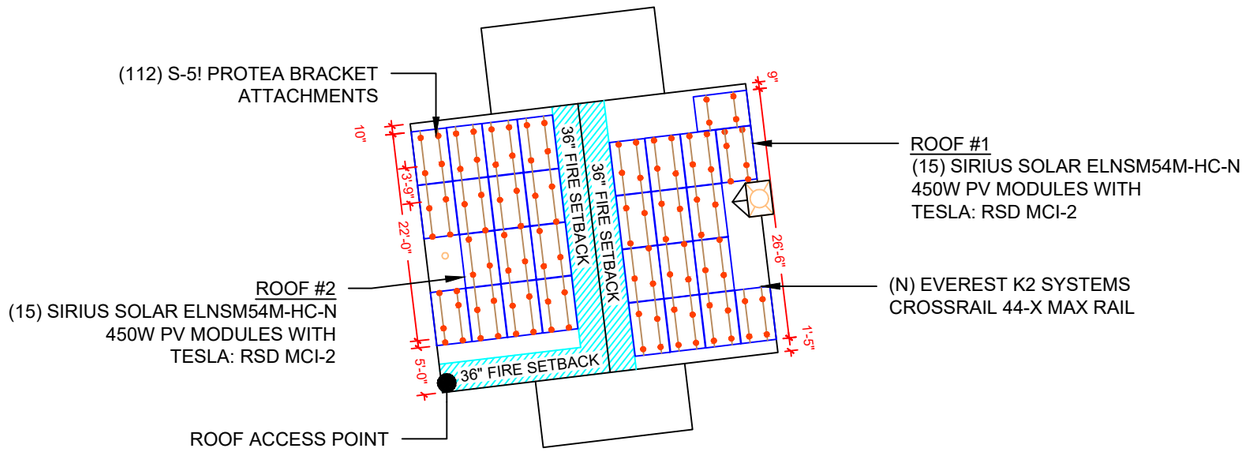

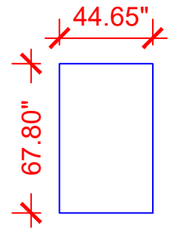

SIRIUS SOLAR ELNSM54M-HC-N 450W MODULES

LEGEND

- VENT, ATTIC FAN (ROOF OBSTRUCTION)
- ROOF ATTACHMENT (DECK MOUNTED)
- RAIL

1 ROOF PLAN AND MODULES
PV-3 SCALE: 1/16" = 1'-0"

TRON SOLAR

TRON SOLAR LLC.
CONTRACTOR ADDRESS:
950 CORPORATE WOODS PARKWAY,
VERNON HILLS, IL 60061
LICENSE #. TGC110144

REVISIONS		
DESCRIPTION	DATE	REV
INITIAL	07/03/2026	A
REVISION	10/12/2026	B

PROJECT NAME & ADDRESS
ELIZABETH L WYER / ETHAN WYER RESIDENCE
203 W STATE ST, FAIRMOUNT, IL 61841
(40.047315, -87.832734)

DRAWN BY
ESR

SHEET NAME
ROOF PLAN AND MODULES

SHEET SIZE
ANSI B
11" X 17"

SHEET NUMBER
PV-3